


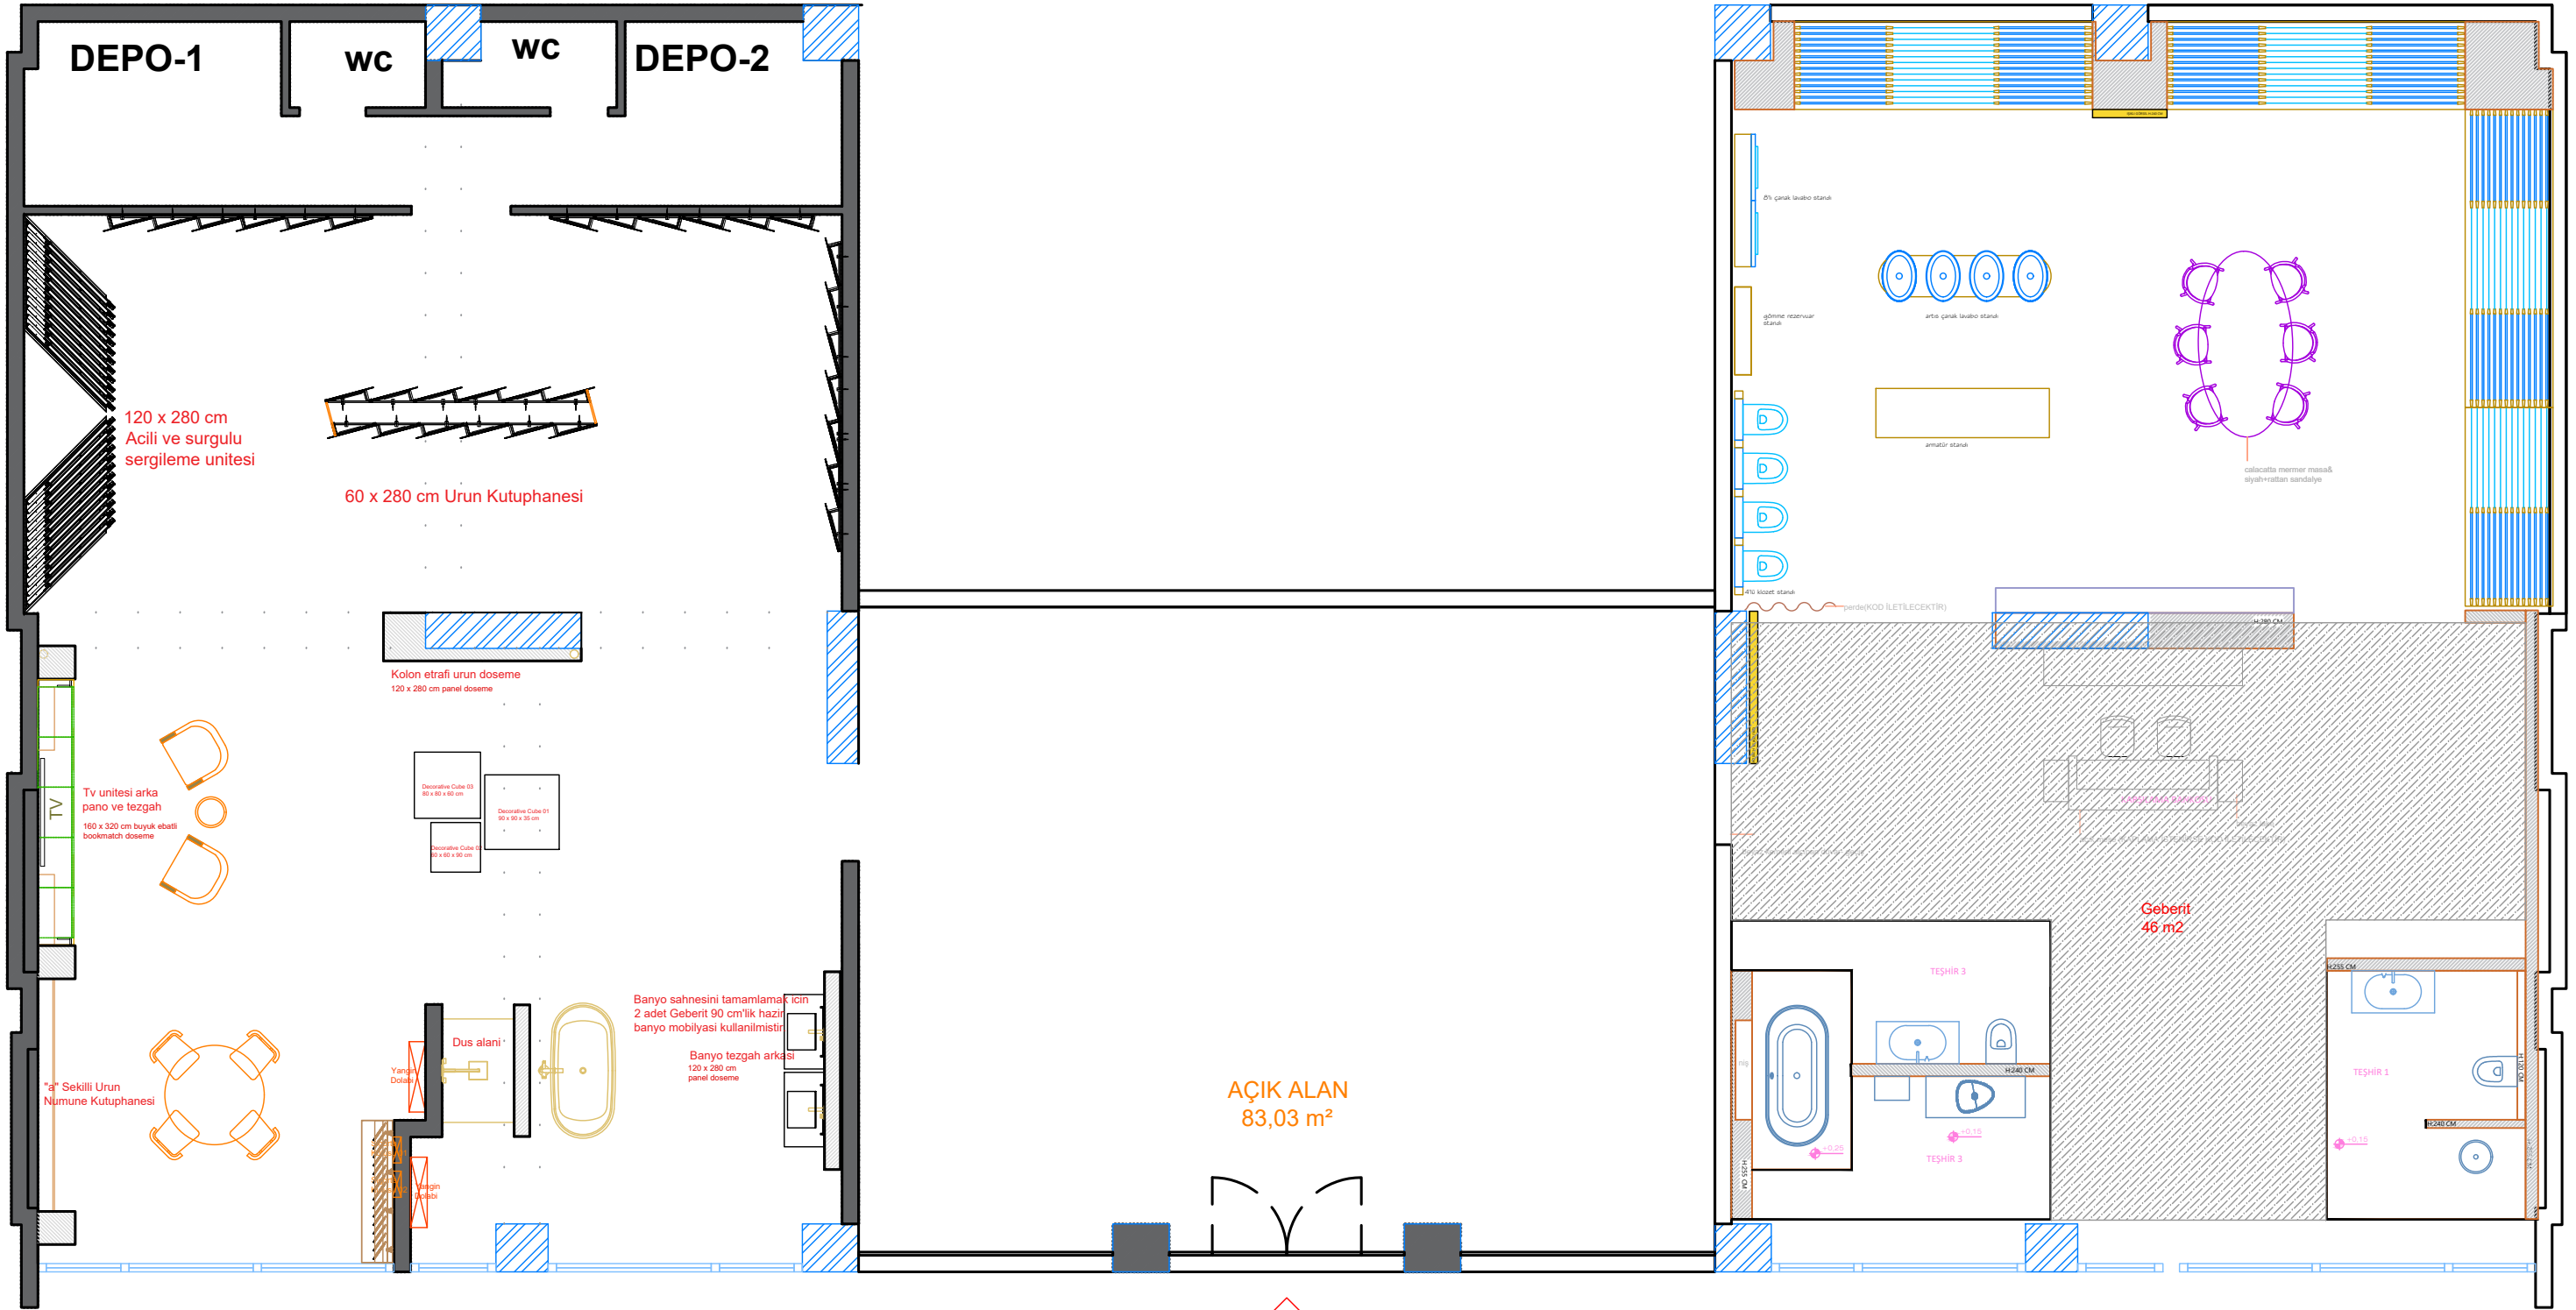

31 adet 60 x 280 cm urun sergileme kapasitesi
 +
 24 adet 120 x 280 cm urun sergileme kapasitesi
 +
 10 adet dosenerek sergilenebilecek urun
 Toplam: 65 farklı urun

GİRİŞ

Project

Anatolia Ekinox Showroom

Title

Layout

Scale

Revision

Printing Date

Notes


anatolia

GENERAL NOTES AND CONDITIONS



ALL DRAWINGS AND SPECIFICATIONS, AS INSTRUMENTS OF DESIGN, ARE THE PROPERTY OF ANATOLIA TILE INC. THEY CANNOT BE USED, DUPLICATED, REPRODUCED OR ISSUED TO THIRD PARTIES WITHOUT WRITTEN AUTHORIZATION FROM ANATOLIA'S INTERIOR & PRODUCT DESIGN TEAM.

ALL DRAWINGS ARE NOT TO BE SCALED.

www.anatolia.com

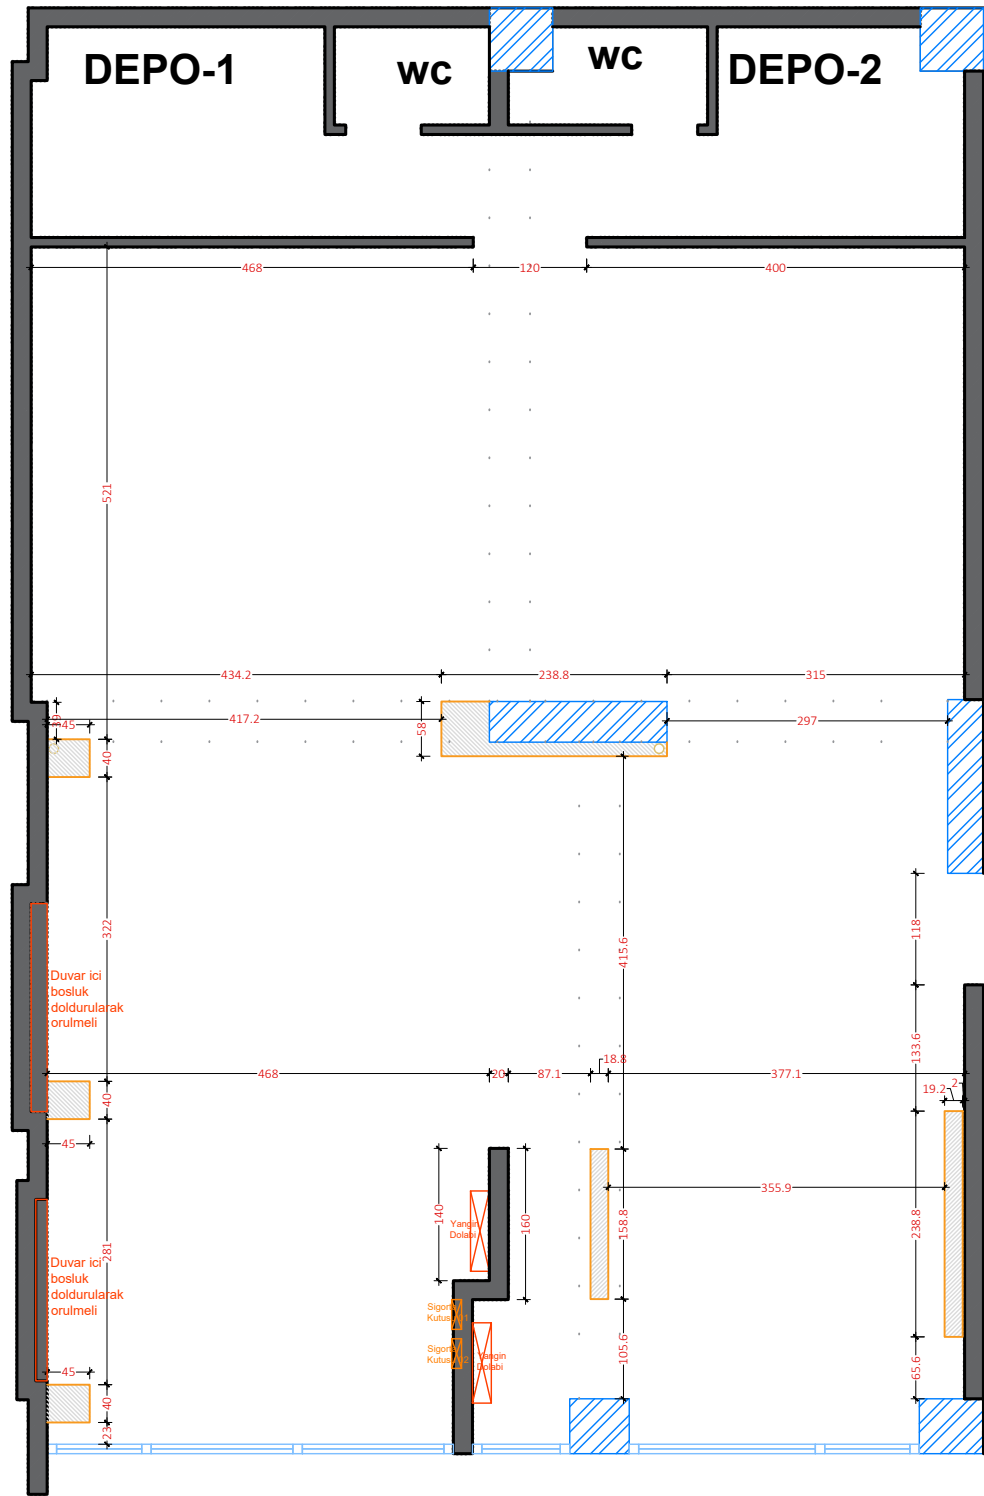

AÇIK ALAN
83,03 m²

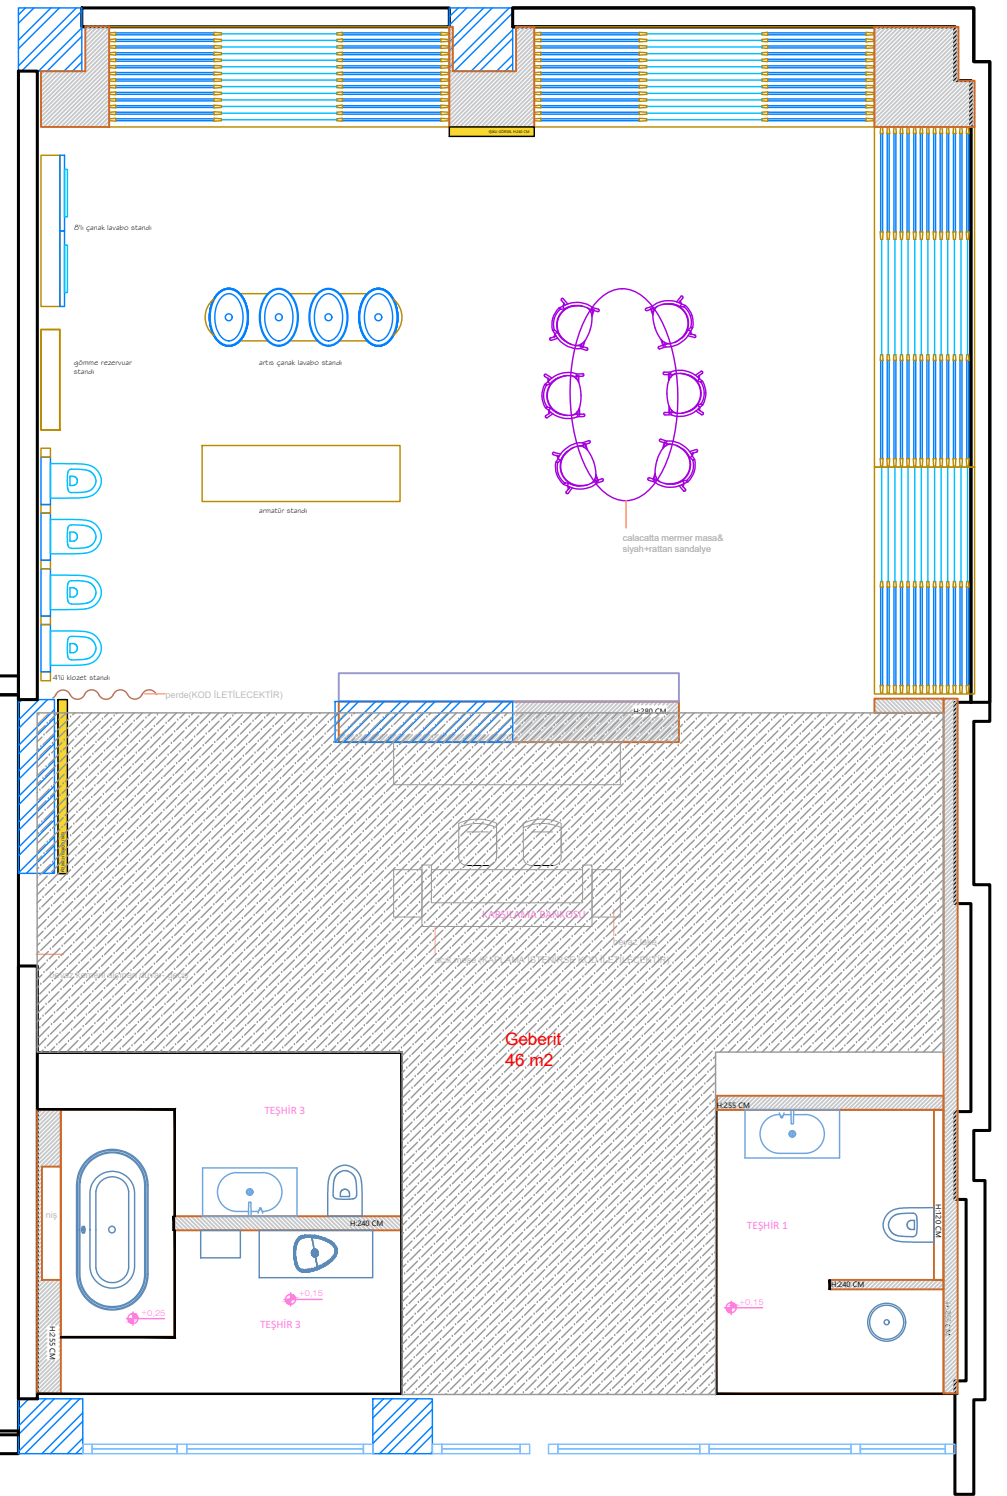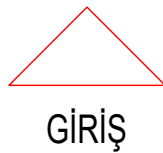

Geberit
46 m²

Project

Anatolia Ekinox Showroom

Title

Wall Dimensions

Scale

Revision

Printing Date


Notes

GENERAL NOTES AND CONDITIONS

ALL DRAWINGS AND SPECIFICATIONS, AS INSTRUMENTS OF DESIGN, ARE THE PROPERTY OF ANATOLIA TILE INC. THEY CANNOT BE USED, DUPLICATED, REPRODUCED OR ISSUED TO THIRD PARTIES WITHOUT WRITTEN AUTHORIZATION FROM ANATOLIA'S INTERIOR & PRODUCT DESIGN TEAM.

ALL DRAWINGS ARE NOT TO BE SCALED.


www.anatolia.com

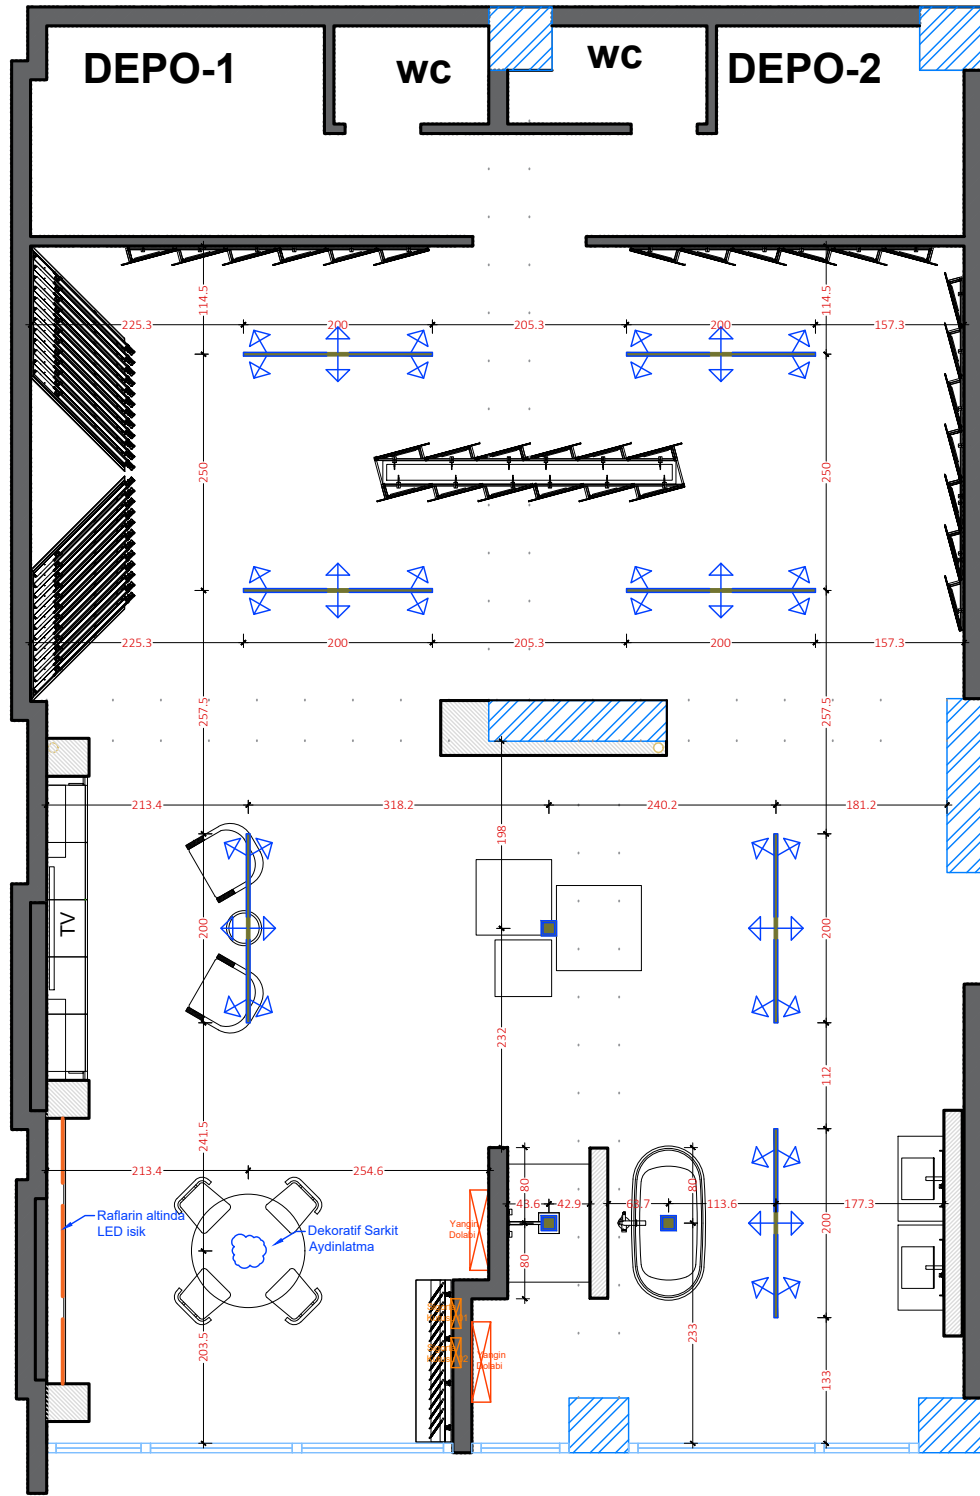

7 adet 2 m'lik ray
42 adet 3500K, 90+CRI Ray spot aydınlatma
3 adet 3500K, 90+CRI Sivaaltı tavanda gomme spot
1 adet dekoratif sarkit aydınlatma
Yaklaşık 12m 3500K kanallı led aydınlatma

AÇIK ALAN
83,03 m²

GİRİŞ

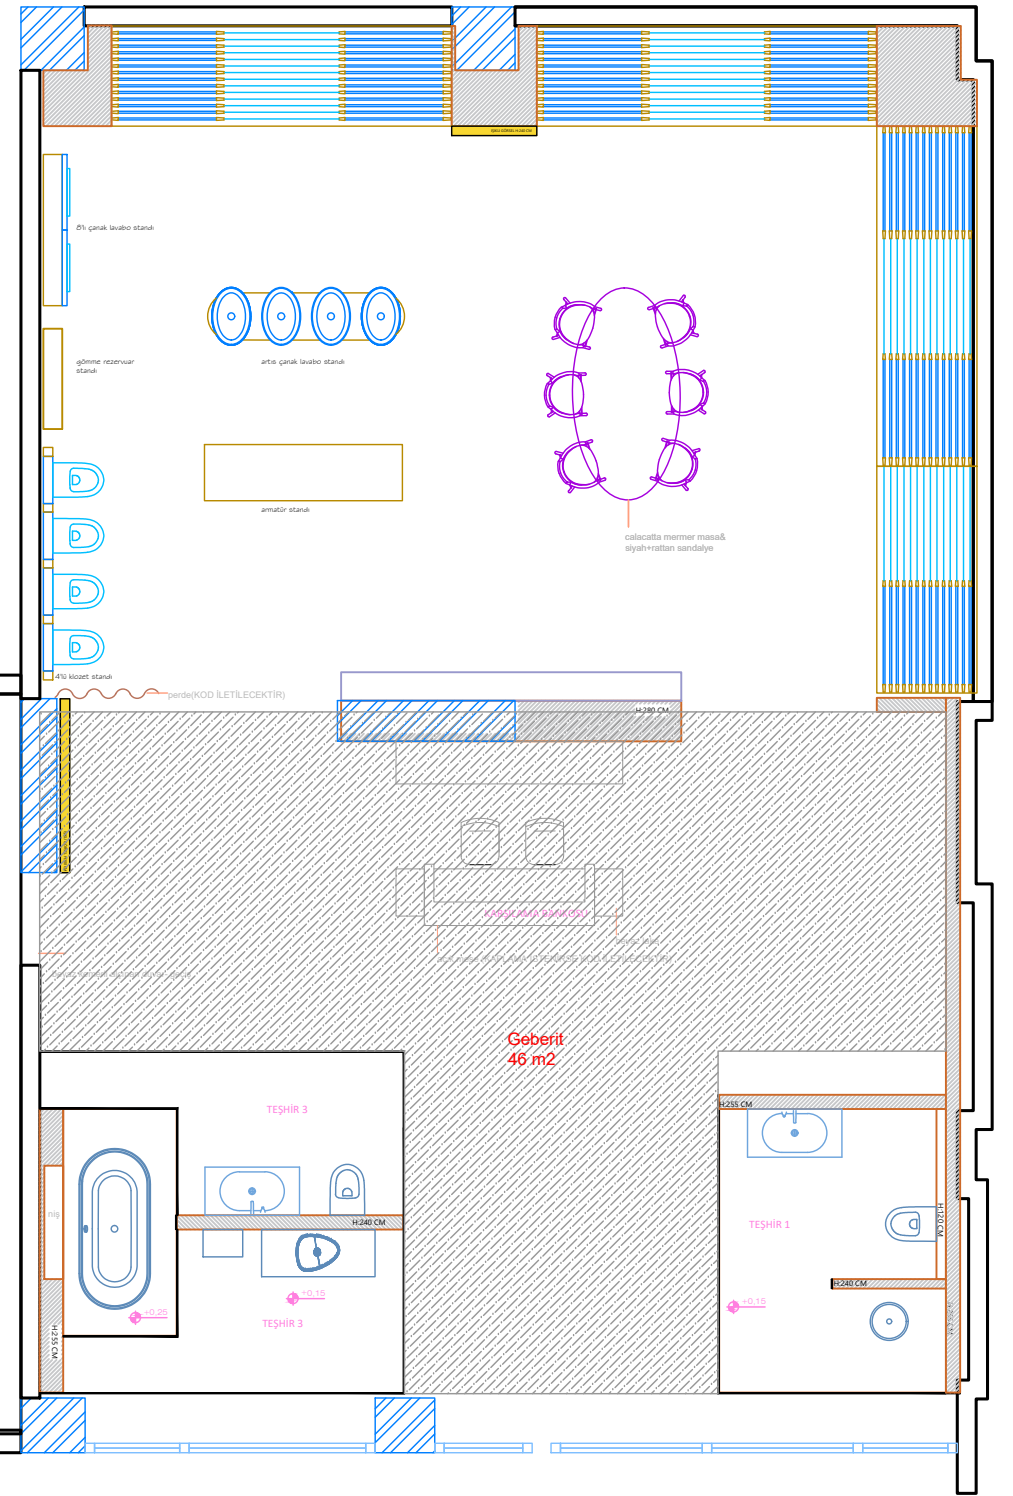

Geberit
46 m²

Project

Anatolia Ekinox Showroom

Title

Reflected Ceiling Plan

Scale

Revision

Printing Date

Notes

GENERAL NOTES AND CONDITIONS

ALL DRAWINGS AND SPECIFICATIONS, AS INSTRUMENTS OF DESIGN, ARE THE PROPERTY OF ANATOLIA TILE INC. THEY CANNOT BE USED, DUPLICATED, REPRODUCED OR ISSUED TO THIRD PARTIES WITHOUT WRITTEN AUTHORIZATION FROM ANATOLIA'S INTERIOR & PRODUCT DESIGN TEAM.

ALL DRAWINGS ARE NOT TO BE SCALED.

www.anatolia.com